

R A H W A   E P H R E M  
S E L E C T E D   P R O J E C T S

2 0 2 4





Or  
[rahwaem.github.io](https://rahwaem.github.io)  
LinkedIn: Rahwa Ephrem  
+251 913 598 115  
[rahwa.emebratu@gmail.com](mailto:rahwa.emebratu@gmail.com)

# Rahwa Ephrem

## INTERMEDIATE ARCHITECT

### Objective

I am an intermediate architect with an experience of an academician as well as a practitioner in the field of Architecture. I wish to devote my career to an in-depth understanding and vibrant expressions I know architecture can create. In my journey towards the role of a senior architect I can leverage my deep understanding of design, construction, and project management to create innovative, high-quality buildings. Driven by a passion for architectural excellence, I am dedicated to continually refining my skills in 3D rendering, sustainable design, and client relations. Each project I undertake is a step towards becoming a master builder and one of the best in the field.

### Education

2011 to Feb 25 2017

**Mekelle University**  
**BSc in Architecture**

Graduated with a CGPA of 3.09

### Teaching experience

2017 – 2020

**MEKELLE UNIVERSITY**, Mekelle, Ethiopia  
**Assistant lecturer** School of architecture and urban planning

- Basic design | Deviation
- Basic design II
- Appropriate building technology alongside Assistant professor Dominika Batista | Timeless shelter 777
- Fundamental architecture for department of civil engineering
- Architectural science III HVAC
- Basic architectural design I

Sep 2021-  
July 2022

**ARBAMINCH UNIVERSITY**, Arba minch, Ethiopia  
**Assistant lecturer** Department of architecture and urban planning

- Urban architecture I
- Introduction to landscape
- Advanced landscape

### Practicing experience

Mar-Jul 2015

**Narga consulting architects and engineers**. Addis Ababa, Ethiopia.  
**Internship** Floor plan designs and modifications, 3D visualization, TOR preparation and bidding

Aug 2022 –  
Feb 2023

**Lodge design**. Bonga, Ethiopia  
**Freelance architectural design** Consulting and 3D production

Mar 2023 –  
May 2024

**Corapita consulting architects and engineers**, Addis Ababa, Ethiopia.  
**Intermediate architect** CAD, 3D form exploration, consultations, initial BOQ preparation, construction permission

May 2024-  
current

**Self-employed**, Addis Ababa, Ethiopia  
**Interior design** renovation of an apartment

### Certifications

April 2016

**MEKELLE UNIVERSITY AND UNLIMITED JAKUB CIGLER ARCHITEKTI**  
Certificate of completion of architectural design workshop for low-cost design and communication

Dec 2016

**ETHIOPIAN INSTITUTE OF TECHNOLOGY- MEKELLE**  
Certificate of participation on the 'Future cities and our cities future' workshop

2018-2019

**ETHIOPIAN INSTITUTE OF TECHNOLOGY- MEKELLE**  
MSADT studio renovation & design- team building project

Aug 2020

**APPASAHEB BIRNALE COLLEGE OF ARCHITECTURE, SANGLI**  
Certificate of participation for the international webinar series on Highrise: planning and technology perspective

Sep 2020

**KONGUNADU COLLEGE OF ENGINEERING AND TECHNOLOGY**  
Certificate of participation for a one-day online webinar on application of lean management in construction industry

### Publications

2016

**Building sustainable dairy business for the case of Gamra, Ethiopia** | MEKELLE UNIVERSITY AND UNLIMITED JAKUB CIGLAR ARCHITEKTI

2016

**77 projects for Mekelle, Ethiopia** | PhD. Dr Dominika Batista.

2018

**TIMELESS SHELTER 777: 71 PROJECTS FOR ETHIOPIA**

---

**Professional training on related fields**

Aug 2009	<b>SOLMINET INFORMATION TECHNOLOGY</b> Completion of non-formal TVET program in basic computer training
Sep 2011	<b>ABYSSINIA FINE ARTS &amp; VOCATIONAL TRAINING CENTER</b> Completed basic drawing and painting practice

---

**Languages**

Amharic	Native language
English	Proficient
Japanese	Basic

---

**Computer skills**

Microsoft office	Word Excel Power point
Architectural design	AutoCAD Revit Sketchup ArchiCAD
Rendering & visualization	V-ray Lumion Enscape Twinmotion
Graphic design & presentation	Adobe photoshop Adobe illustrator Adobe indesign
3D modeling	Autodesk 3ds Max

**References**

Ato Fikreslassie Abey	Narga consulting architects and engineers   Tel: 0924913000   e-mail: <a href="mailto:narga.consulting@gmail.com">narga.consulting@gmail.com</a>   Website: <a href="http://www.nargacon.com">www.nargacon.com</a>
Ato Mikiyas Tewodros	Conservation & heritage expert at national museum of Ethiopia   Tel: 0906150644   e-mail: <a href="mailto:mikitewo1@gmail.com">mikitewo1@gmail.com</a>   Website: <a href="https://mikiyastefera.github.io/cv/#three">https://mikiyastefera.github.io/cv/#three</a>
Ass. Prof. Dominika Batista	Architect practitioner, founder and CEO of studio db   e-mail: <a href="mailto:dominika.batista@studiodbai.com">dominika.batista@studiodbai.com</a>   Website: <a href="http://www.studiodbai.com">www.studiodbai.com</a>

## OVERALL PROJECT PARTICIPATIONS AT LARGE

Through my internship and practice experience, I am able to participate in numerous projects on different scales including;

### SMALL SCALE

RESIDENTIAL BUILDING  
RESIDENTIAL INTERIOR  
APARTMENT INTERIOR

### MEDIUM SCALE

MIXED USE BUILDING  
OFFICE BUILDING  
APARTMENT BUILDINGS

### LARGE SCALE

AN ECO RESORT  
LARGE SCALE AUDITORIUM

And amongst all here are a few selected projects.



# NATIONAL LOTTERY

## Shashemene , ethiopia

INTERNSHIP | FOURTH YEAR | 2015

The National Lottery for the shashemene branch is a G+4 office building design.

Participation includes:

- TOR preparation
- Submitting the initial bidding documents
- Editing spatial arrangement of the plans
- Preparation of paper works, both legal and for client
- Tracking progress according to agreed schedule
- Tracking subcity progress
- Fencing design for the same project
- Final 3D and rendering
- Toilet design for the gents
- Check payment at 40% design stage





The image on the left is a photo of the stage the building was at where the building was at a stage where fenestration layout was already configured. My job here was to propose a durable and aesthetical facade treatment.

Therefore the proposal is a durable and aesthetical facade treatment which is a ceramic facade system for a weather resistant and easy to maintain in a brick red earthy tones.



# MIXED USE BUILDING

Addis Ababa, Ethiopia | INTERNSHIP | FOURTH YEAR | 2015



# ECO RESORT

Bonga, Ethiopia

FREELANCE | 2022-2023



All floor plan space modifications

3D for layout of the entire compound | spatial organization

Open space street and boundaries that take into consideration the nature of activity of each building including public to private zones

Parking space design



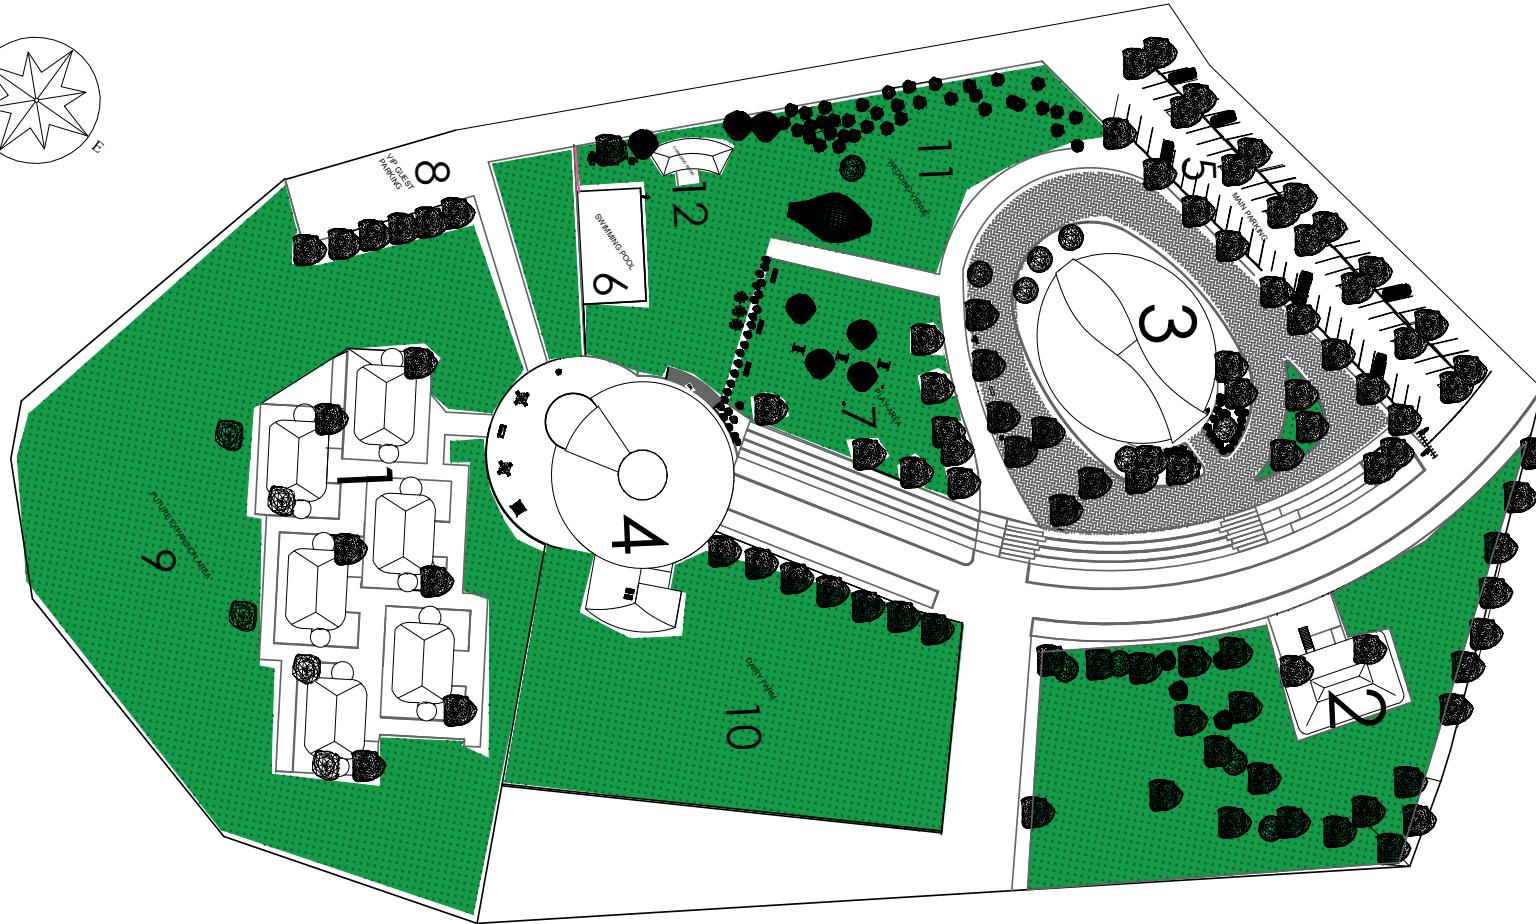
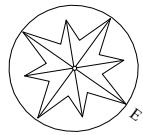


## SITE PLAN


### LEGEND

1. GUEST BED ROOM BLOCKS
2. JUICE HOUSE
3. MEETING HALL
4. RESTAURANT
5. MAIN PARKING
6. SWIMMING POOL
7. PLAY AREA
8. VIP GUEST PARKING
9. FUTURE EXPANSION AREA
10. DAIRY FARM
11. WEDDING VENUE


# Juice house

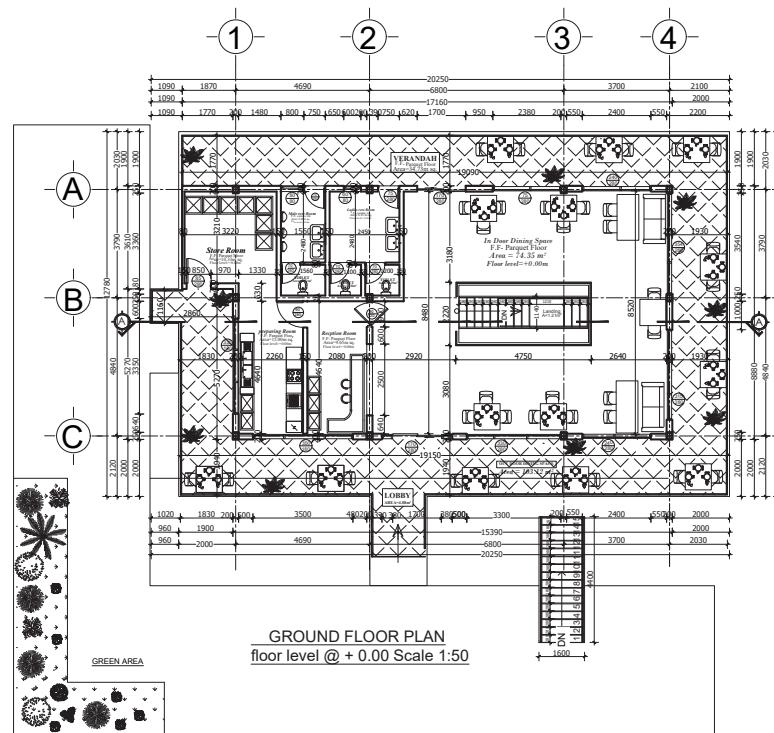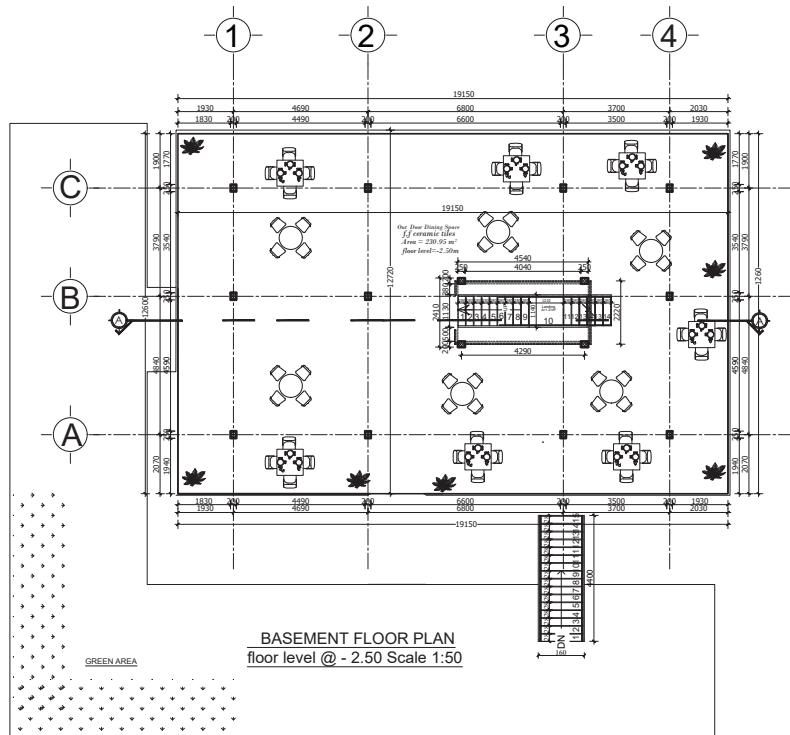


# Meeting hall

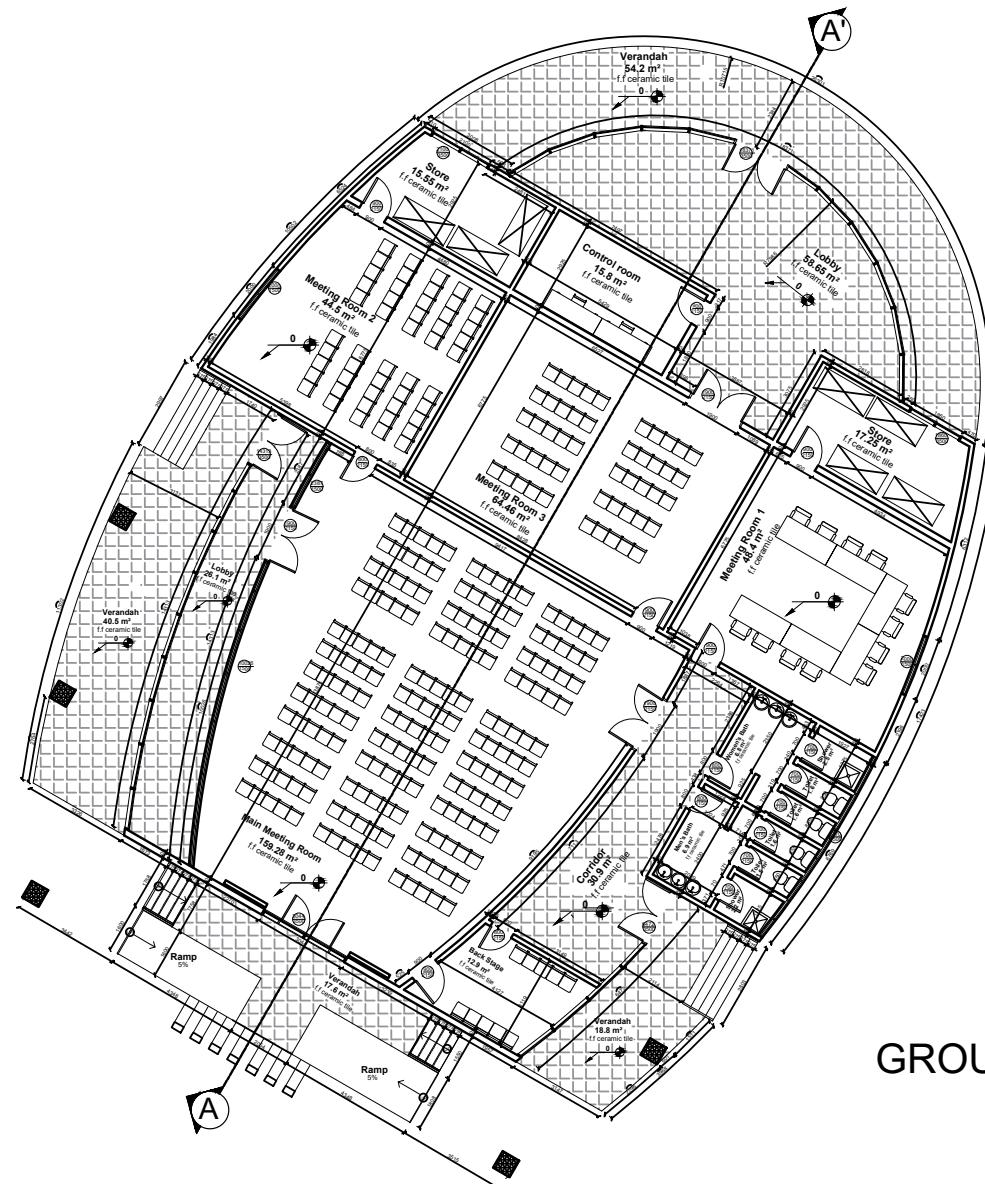

# Restaurant

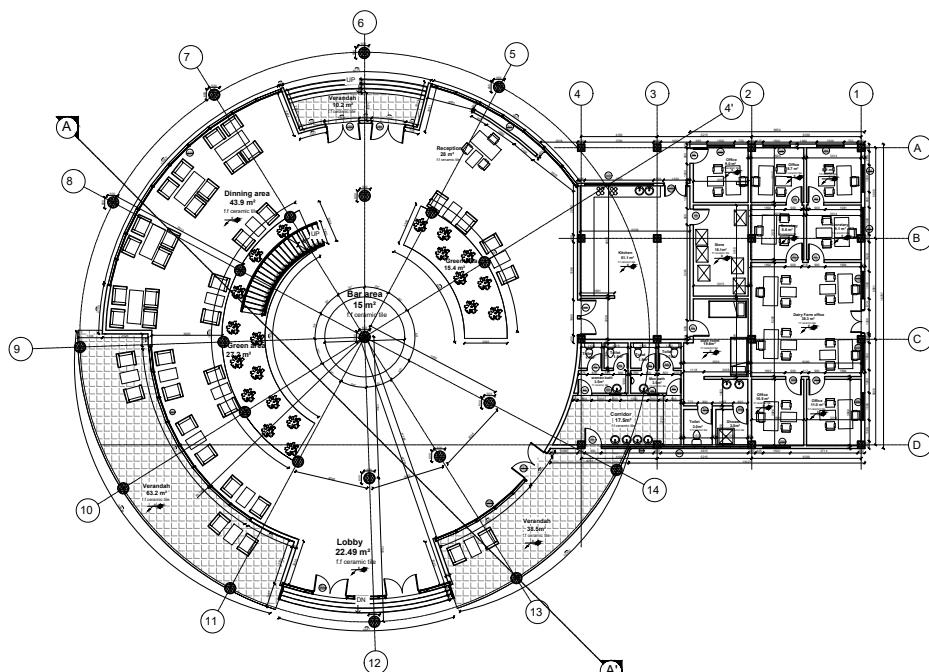


GROUND Floor Plan  
SCALE 1:50

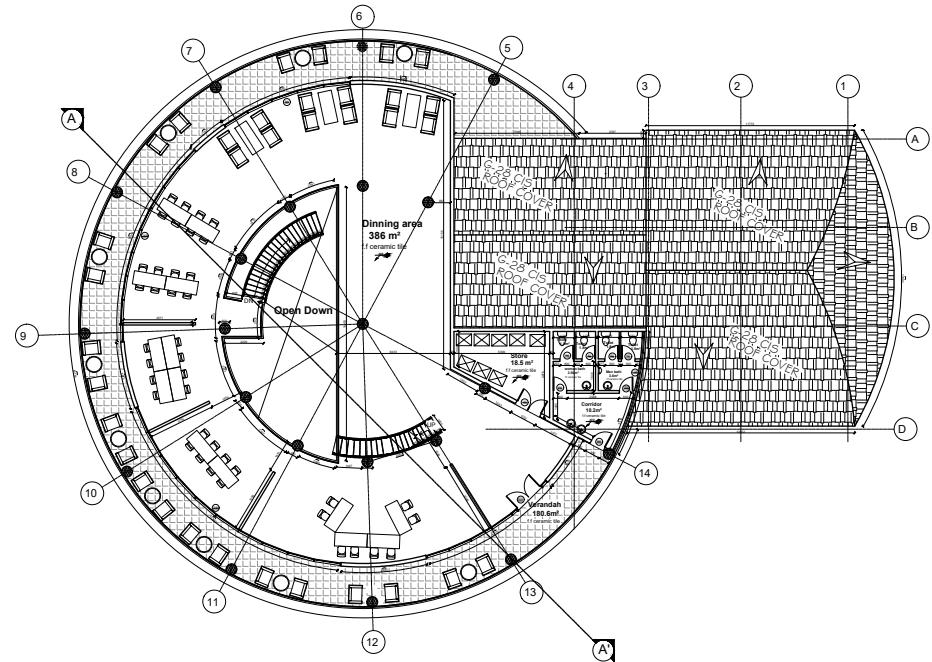


FIRST Floor Plan  
SCALE 1:50

# Guest rooms

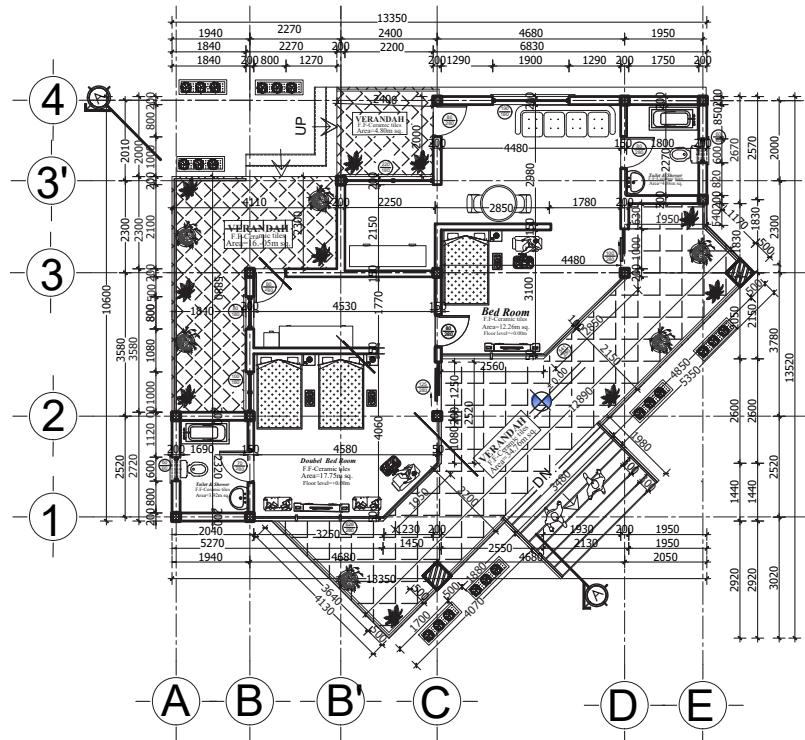

**GROUND FLOOR PLAN**  
floor level @ + 0.00 Scale 1:50

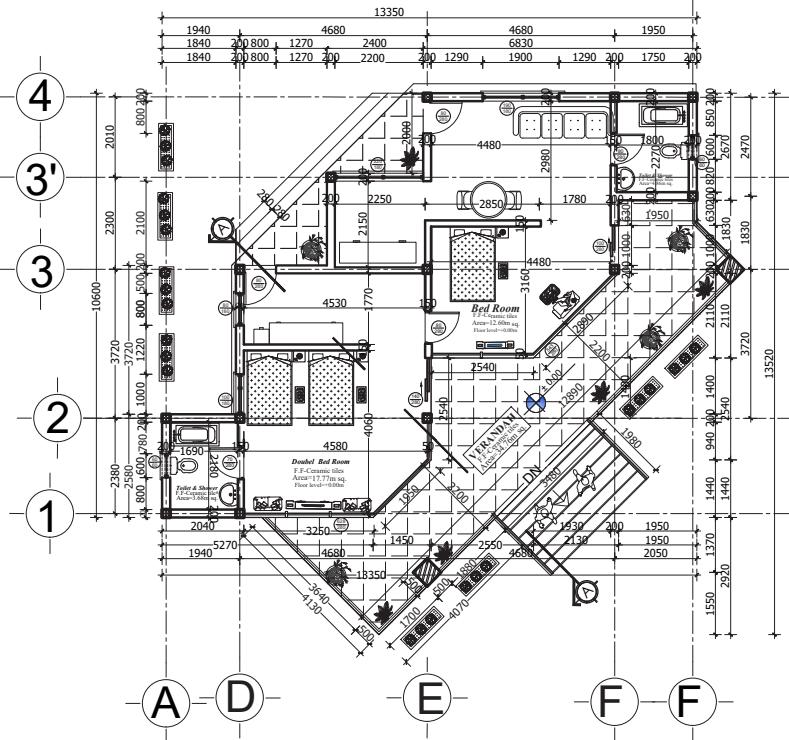

GROUND FLOOR PLAN

# APARTMENT RENOVATION

Addis Ababa, Ethiopia

FREELANCE | MAY 2024 - CURRENT






Major works done are:  
Material selection

Communication and supervision with the workman

# PHOTOGRAPHY MEETS 3D MODELING



Flower species scientific name: Grevillea Robusta

ARCHICAD | AUTOCAD 3D | 3DS MAX

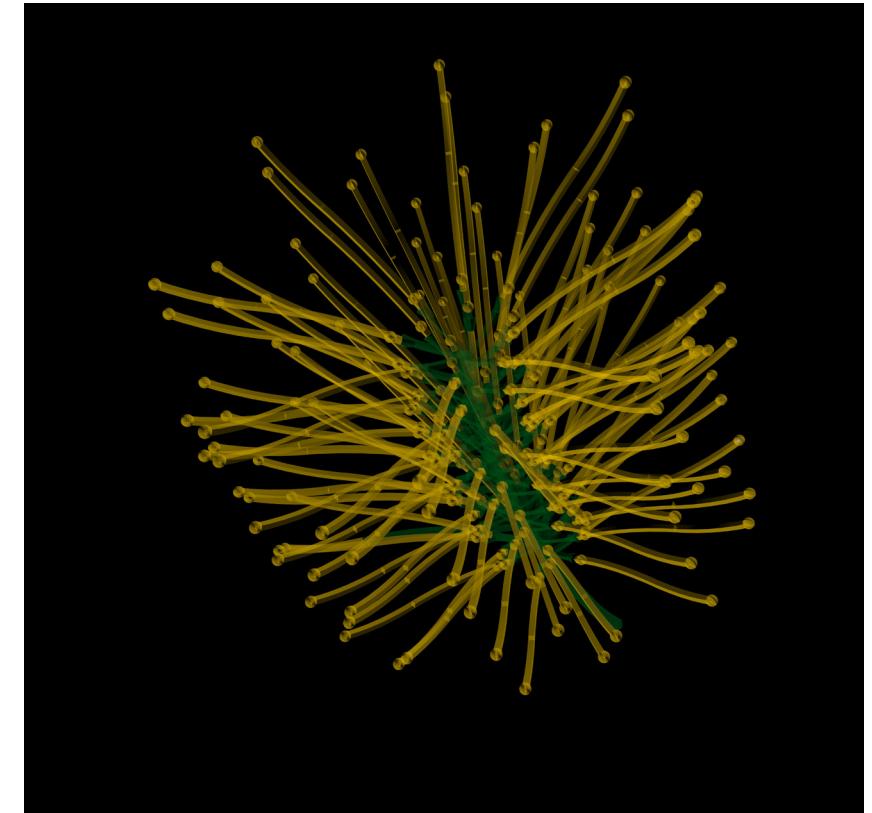

Flower species scientific name: *Mirabilis jalapa*

3DS MAX

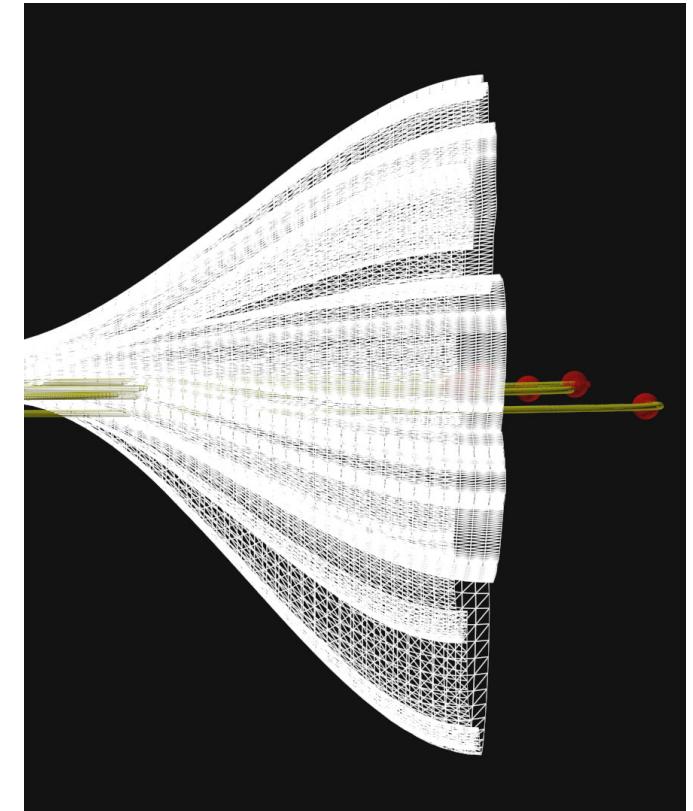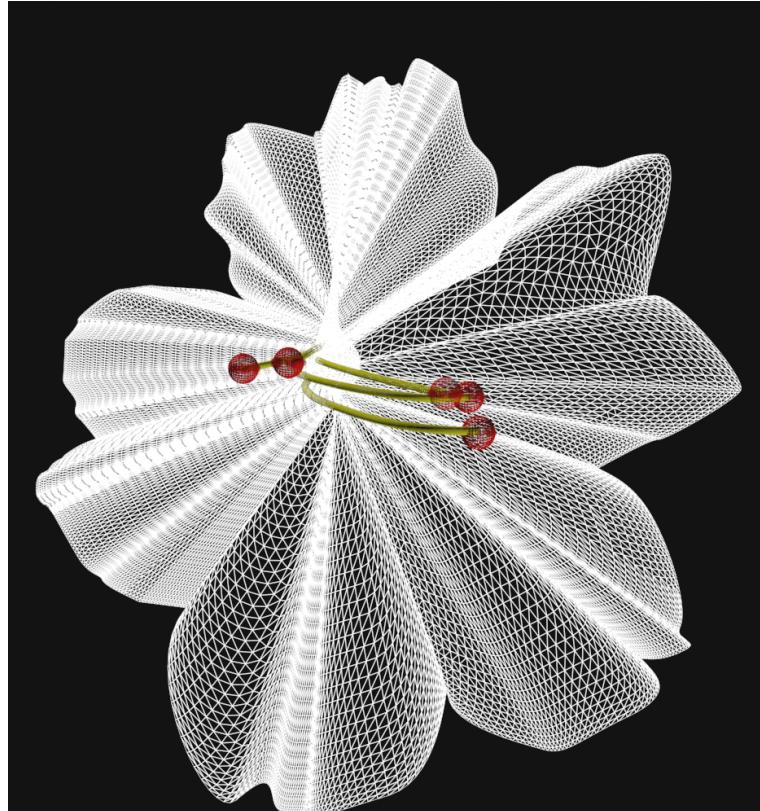

መቻል የፌዴራል  
የረዳተኞች እና አለማ-ናይ ቅልጋት ቤት

Tel: (034) 4407500 or 4407501  
Fax +251344418615  
P.O.Box 231Mekelle,ET  
E-mail: info@mu.cdu.ct



Mekelle University  
Registrar & Alumni Directorate

RefNo MU/169968/2017  
Date:2017-02-25



ለመረጃዎች ሆኖ:

ይህን አኅድን መሠረት በ "የ ፈ ምርመራ ባቻል የፌዴራል  
በረዳተኞች" በ ዓ.ም. 18, 2017 ቀን በመተዳደሪያው ይህ  
ማኅበር ወረቀት ተመርምናል፡ ወርሃዊ ወጪውን  
በአጠቃላይ 3.09 መሠረት ስምምነት፡ የሚመለከት ይመለከታል  
የጊዜዎችን በዋጥና መሠረት ወቅት መሠረት የሚመለከት ይመለከታል  
ስለጠና የሚመለከት ይመለከታል፡

To Whom It May Concern:

This Certificate is issued to Rahwa Ephrem Mehratu upon his/her graduation with B.Sc in Architecture (Regular) Undergraduate Regular on 2017-02-25G.C He/She scored a CGPA of 3.09. The Original Diploma and Transcript will be issued upon discharging cost sharing responsibility.


Registrar & Alumni Director  
የረዳተኞች እና አለማ-ናይ ቅልጋት ቤት





የኢትዮ አዲስ አበባ ከተማ አስተዳደር ትምህር ሲ.ኤ

CITY GOVERNMENT OF ADDIS ABABA  
EDUCATION BUREAU

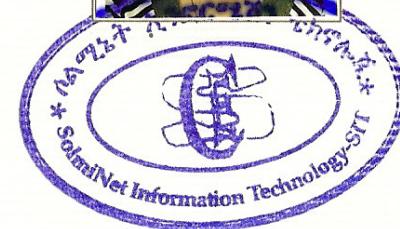

የምሳክ ወረቀት  
CERTIFICATE

ለ ሚ.ቁ.፳፻፱፭

መደበኛ ባለሙያው ተ/መ/ት/ሥ/ ጥርጋዬ በስልጣኑት አንድርሱን  
ቴክኖሎጂ (ኤ.ት) ማዋልበኝ ማስከላ በመሠረታዊ የከምጥያቶ መ.ያ

ለ ሚ.ቁ.፳፻፱፭ ወረቀት የተሰጠውን ሥልጠና በማጠናቀቅ/ቁ

ይህ የምሳክ ወረቀት ተሰጥቶታል/ቁ/ል/፡፡

ቀን: ዓ.ም. 29, 2001

የከፍል ከተማው አስተዳደር ሲ.ኤ  
Sub-City AMBAKU TIBEBE MEKONEN  
Education Office Head, P.O. 216.  
Education Department Head



THIS CERTIFICATE IS AWARDED TO

RAHWA EPHREM

IN THE COMPLETION OF NON FORMAL T.V.E.T. PROGRAM

FOR Three MONTHS IN BASIC COMPUTER  
TRAINING AT *SOLMINET INFORMATION TECHNOLOGY*  
(SIT).

Date: 05 AUGUST 2009

ባለቤር አሽብር  
የፍ ሥራ አሽብር  
Balnjer Ashebir  
General Manager

የማዋልበኝ ማስከላ አስተዳደር  
Coordinator of the Training Institute

# አዲስ ኢያን የሥነ- ትቦብና የመ-ያ ማዕድልዎች ተቋም ABYSSINIA FINEARTS & VOCATIONAL TRAINING CENTER



መርተኞች

ለ-፲፻፲፭ ዓ.ም.

በአዲስ ኢያን- ትቦብና መ-ያ ማዕድልዎች ተቋም  
አመካኝነት ለ፲፻፲፭: ወጪ-፭  
የተሰጠውን የሚፈጸመውን በለምዶች ሥልጣን/  
ተግባሪ ተቋር በሚገባ ስለሆሙኑን ይህ  
መርተኞች ተሰጥቶታል/ቻል::

የአዲስ ኢያን- ትቦብና የመ-ያ  
አዲስ ኢባባ: ኢትዮጵያ

Genet Kebede

Manager

ማዕድልዎች ሥራ አስተዳደር  
Manager of the Training Center

To - RAHWA EPHREM

is awarded this certificate for successfully  
Completing - TWO MONTHS  
training/ practice and theory/ in DRAWING &  
PAINTING which has been conducted by  
ABYSSINIA FINE ARTS & VOCATIONAL  
TRAINING CENTER

Date Sep 6 2011

Addis Ababa, Ethiopia

WORKTEAM  
Senior Instructor &  
Painting Dept. Head

የሥነ- ትቦብና  
Training Coordinator



TO SUPPORT CREATIVITY, INNOVATION AND DYNAMIC LOW-COST AND SUSTAINABLE DESIGN, TO TRANSFORM THE EXISTING POTENTIAL INTO SOMETHING VITAL AND RADICAL IN A DECENT AND APPROPRIATE WAY, TO QUESTION THE ROLES OF ACTORS AND TO REVIEW ITS DISTRIBUTION, TO EVALUATE THE ACCESSIBILITY AND AVAILABILITY OF THE DESIGN TO FIND WAYS HOW TO PERCEIVE, UNDERSTAND AND DEAL WITH LOCAL WEALTH AND PEOPLE'S NEEDS, HOW TO ACTIVATE REMOTE AREAS, HIDDEN SPOTS, HOW TO TURN THEM INTO THE PLACES OVERFLOWING WITH UNIQUENESS AND INSPIRATION, HOW TO ATTRACT THE PEOPLE TO CARE ABOUT IT, HOW TO THINK PROGRESSIVELY AND SUSTAINABLY, HOW TO CONTRIBUTE TO THE DEVELOPMENT, HOW TO RESPOND TO THE ASPIRATION OF PEOPLE.

HOW TO USE LOCAL MATERIALS, HOW TO USE SECONDARY MATERIALS - HOW TO RECYCLE, HOW TO MAKE THE COMMUNITY FEEL THE OWNERSHIP, ARCHITECTURE AS A CONTRIBUTION TO THE DEVELOPMENT, FINDING FOCAL POINTS OF COMMUNITY ATTENTION, PHENOMENS AND ARCHETYPES, COMMUNICATION SKILLS AND PRESENTATION TECHNIQUES...

MATERIAL REGENERATION, FINDING FOCAL POINTS OF PUBLIC ATTENTION, PHENOMENA AND ARCHETYPES, COST MINIMIZATION, AFFORDABILITY, REPPLICABILITY, MATERIAL SELECTION, FLEXIBILITY, USER SELECTION, EFFECTIVE CONSTRUCTION TECHNOLOGIES PRESENTATION TECHNIQUES, COMMUNICATION...

MEKELLE UNIVERSITY AND UNLIMITED JAKUB CIGLER ARCHITEKTI  
ISSUE TOGETHER

# CERTIFICATE OF COMPLETION

OF WORKSHOP ABOUT ARCHITECTURAL DESIGN

ORGANISED IN MEKELLE FROM 18<sup>TH</sup> TO 26<sup>TH</sup> APRIL 2016

CALLED

## LOW COST DESIGN AND COMMUNICATION

TO RAHWA EPHREM

WHO SATISFACTORILY PARTICIPATED  
AND COMPLETED THE WORKSHOP



GEBREMESKEL KAH SAY, PhD.  
SCIENTIFIC DIRECTOR

EiT-M

SARA AMARE GEBREMESKEL,  
HEAD, SCHOOL OF ARCHITECTURE  
AND URBAN PLANNING

Ethiopian Institute of Technology – Mekelle  
University  
Ethiopia



MICHAELA SOLNICKÁ VOLNÁ, Ing. Arch.  
WORKSHOP ORGANISATOR AND TUTOR

Unlimited. jakub cigler architekti  
Architecture within human commitment

AWARDED IN MEKELLE, APRIL 27, 2016

MIYAZYA 18, 2008

Folmida Michaela

THE WORKSHOP IS DEMAND-DRIVEN PROJECT BASED ON IDENTIFICATION OF NEEDS OF THE FACULTY. IT IS A COMPLEMENT OF THE COURSE ARCH 5422 LOW-COST STRATEGIES IN DESIGN FOR 5TH YEAR STUDENTS IN THE PROGRAM B.Sc. IN ARCHITECTURE. THE AIM OF THE COURSE IS TO TEACH AND TRAIN LOWCOST STRATEGIES IN DESIGN. STUDENTS SHALL BE ABLE TO ADOPT LOW-COST STRATEGIES IN THEIR DESIGN PROJECTS BASED ON INTERNATIONAL AND ETHIOPIAN EXPERT KNOWLEDGE.



Date : 26/8/2020

Shri. Vasantaro Banduji Patil Trust's

## Appasaheb Birnale College of Architecture, Sangli International Webinar Series on

# Highrise : Planning and Technology Perspective 2020

## *Certificate of Participation*

E- Certificate GZTAK8-CE000084

This e- certificate Presented to Rahwa Ephrem Mebratu  
Designation Graduate Architect From Mekelle University  
for attending Webinar on " Highrise : Planning and Technology Perspective 2020 " organized by  
Appasaheb Birnale College of Architecture , Sangli On 24 th To 26 th August 2020.

**GUEST SPEAKER**  
Ar. Virag Sarode  
Senior Project Architect ,from USA

**GUEST SPEAKER**  
Ar. Kashmira Sarode  
Senior Architect ,from USA

**GUEST SPEAKER**  
Ar. Ashish Kalkar  
Senior Architect ,from Dubai,UAE

**CO-ORDINATOR**  
Er. Pravin Pise  
Associate Professor

**CO-ORDINATOR**  
Ar. Shantanu P. Jagtap  
Associate Professor

**CONVENER**  
Ar. Vijay B. Sambrekar  
Principal



# Kongunadu

College of Engineering & Technology  
[Autonomous]

An Autonomous Institution Affiliated to Anna University, Approved by AICTE, New Delhi, Chennai, Accredited by NBA,  
Accredited by NAAC B++ Grade, Recognized by UGC with 2(f) & 12(b), ISO 9001:2015 Certified Institution.  
Namakkal - Trichy Main Road, Tholurpatti Po, Thottiam Taluk, Trichy Dt - 621 215



## DEPARTMENT OF CIVIL ENGINEERING

### Certificate of Participation

This is to certify that Dr./Mr./Ms. Rahwa Ephrem Mebratu of **Mekelle University** has attended One Day Online Webinar on "**APPLICATION OF LEAN MANAGEMENT IN CONSTRUCTION INDUSTRY**" organized by Department of Civil Engineering, Kongunadu College of Engineering and Technology, Thottiam on 01/09/2020.

**HoD/Civil**  
Dr. S. Kavipriya.

**Dean(R&D)**  
Dr. J. Yogapriya.

**Principal**  
Dr. R. Asokan.



ΦΤC/Ref.No: E18-m/18294/12  
Φ?/Date:

**ለደር/ከተ/ወ/ሮ/ወ/ሪት እኩዎም መብርቱ**

σο. Ε

ԴԻԲԻ ԲՆԴՈ ՈՉ ԹԱՐԱ ՃՎԵՔ ՏՎԱՅ ՄԱՍԻ ՀԵՄԱԴԻ ՀԵՄԱԴԻ

እርሱም በወጪ ይጠናል፡ የኢትዮጵያ ኢንስቲትዩት-መዋለ ደረሰኝ ሌከተር የስራ መደብ  
በቁጥሩት ተቀጥረው በመስራት ጥሩ መሆኑም ይታወቂል፡ በመሆኑም በእናሳ የሰነድ ስርዓት ከሚገኘ ለከፍተቶ  
ተሞህርት ተቁጥሩ የወጪው የኩጥብ ሲሆን ምክንያት /JPEG/ መስራት የየዘተኛ የስራ መደብ በ XIV ደረሰኝ  
የተደረጋጀ መሆኑን እንዲታወቂት እንደገኘለን፡



Getachew Gebru Dejenea  
Human Resource Coordinator

፭፻፻፯

- > ለሰደንትልኩ የይፈከተኬ ዕ/ቤት
  - > ለምክትል ለደንትልኩ የይፈከተኬ ዕ/ቤ
  - > ለማኝቸዋን የይፈከተኬ ዕ/ቤት
  - > ለምክትል ማኝቸዋን የይፈከተኬ ዕ/ቤት
  - > ለሰው የብት ስራ አመራር ዕ/ቤት
  - > ለፏይናንስ እና በቃት ስራ ክፍል
  - > ለእርከቶችና ክተማ ጥሩን ትኑት

$\lambda_1, \lambda_2, \lambda_3 - \sigma^0$



P.O.Box 21  
አርባ ሙንጻር ኢትዮጵያ  
Arba Minch, Ethiopia

አዲስ የማኑያዊ የኢትዮጵያ  
ARBA MINCH UNIVERSITY  
ተክኖሎጂ አ.ካነት-የት  
INSTITUTE OF TECHNOLOGY  
የግ/ ሌጭታዊ የይሬክተር ዘመን  
DEPUTY SCIENTIFIC DIRECTOR OFFICE

PTC: AMIT/D/S/D/14  
Ref. No.  
Date: 30/6/2014 9.90

ՕՀԻ/Դ/Պ/Պ/ՏԵՇՈՒՑ Տ/Ա

A.90. P:-

ԴՔԲ :- հսովա բնիկների քառ տղանեցն ըստիւթեա:

հՀՅԱՀ-ԹՎՈՎ ՍՄԵՐ-ԻՆ ԱՐԺՈՒՆՈՎ ԽՈՒԴԻ ԽՈՎԱԾԱԿ ՄՊԳՄԵՐ-Ն աՅ  
ՔԱՌԱԾԱ-ՔՐԴ-Ն ԱՇԽԱՎՈՒ ՄՊԸՆԳ-ԹՎ Ք-ՓՓԱԱ ԱՄՄՐ-Դ ԱՀՆԵՐ-ՔՐԴ-Ն  
ԱԿԵՒԵՒԾԸ ԻՒ-Պ ՏԱՅ ԿԱԼ-Ի ԻՒ-ԸՆԳ-Դ ՄՊԳ-Ն ՏՈՒԽԱ ՈՊԳ-Թ ԻՒ-Ք Ք-ՊՈՒԾ  
13 ՄՊԳՄԵՐ-Ն ԱՄԸ ՊՈՒ-ԹՎ ԱՅ ՔՐԴ-Ա ԱԼՄՐ-Պ ՄՊԳՄԵՐ-Ն ԱՄԸ ՊՈՒ-ԹՎ ԱՅ  
ՄՊԸՆԳ-ԹՎ Դ-ԱԾ ԱՀՆԵՐ-Ը Դ-ՎՍԸՆ-Դ Պ-ՆԵՐ-Ը Ք-ՆԵՐ-Ը Ք-ՆԵՐ-Ը ՄՊԸՆ-Դ Ա-Ծ-Դ  
Ք-ՆԵՐ-Ը Ա-Ծ ՀՀՅԱՀ-ԹՎՈՎ ԱՄԸՆ-Գ-Գ ԱԿՈՒ հԿՈՒ ԱՄԸ ԱՅ ՄՊԸՆԳ-ԹՎ Ը-ՎԸ Ա-Ծ-Դ  
Ք-ՆԵՐ-Ը ՄՊԸՆ-Դ Դ-ԱԾ ԱՀՆԵՐ-Ը ՀՀՅԱՀ-ԹՎՈՎ Ա-Ծ-Դ ՀՀՅԱՀ-Գ-Գ Հ-ԱԾ-Դ Ք-ՆԵՐ-Ը

- |                  |                   |
|------------------|-------------------|
| 1. መ/ት በተከለ ወርቅ  | 8. መ/ር ካኝበል እንዳለ  |
| 2. መ/ት ቁልከያን በሰኔ | 9. መ/ር ይርጥ ከላቸ    |
| 3. መ/ር አዲስ ነኑ    | 10. መ/ት ላህወ እኩልያዎ |
| 4. መ/ር አልፏዴሮ ባይ  | 11. መ/ት ሲባሽ ገብሩንስ |
| 5. መ/ር የሰጠ የማና   | 12. መ/ር አካላለ ደሳለኝ |
| 6. መ/ር የርዳምስ አያለ | 13. መ/ር ይዋጥ አነፃው  |
| 7. መ/ት ቁጻዕት ስያለ  |                   |

709T/

- ለማይገኘትኩና የ/ሽ/ዕት
  - ለምግባርኩና/የ/ሽ/ዕት

290 di 2



ሰላምና ንግድ ታደሰ (Ph.D)  
Solomon Neway Jida (PhD.)

Ph.D. to AMIT  
Dep. Scientific Director, AMIT



**EiT-M**

Ethiopian Institute of Technology - Mekelle  
የኢትዮጵያ ገንዘብ አኋላ ቤት - መሆኑ  
Mekelle university  
መቀበ የሚከተሉት


# CERTIFICATE OF PARTICIPATION

PROUDLY PRESENTED TO

RAHWA EPHREM

FOR HIS/HER PARTICIPATION ON THE  
'FUTURE CITIES AND OUR CITIES FUTURE'  
WORKSHOP

AS PARTICIPANT FROM DECEMBER 15 TO 17,  
2016 ORGANIZED BY THE SCHOOL OF ARCHITECTURE AND  
URBAN PLANNING.

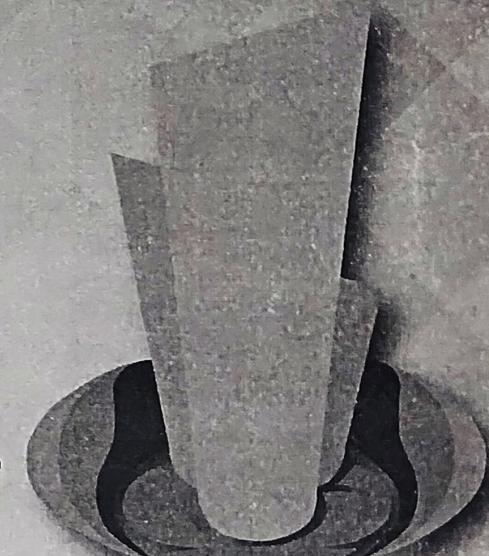

FUTURE  
OUR **CITIES** FUTURE  
NATIONAL WORKSHOP  
2016

PLANNING  
Sara Amare Gebremeskel  
Head, School of Architecture &  
Urban Planning  
*[Signature]*

HEAD, SCHOOL OF ARCHITECTURE  
AND URBAN PLANNING



CHAIR HEAD,

*[Signature]*

URBAN PLANNING  
Teshaye Legesse  
Chair Head of Urban Design  
*[Signature]*

